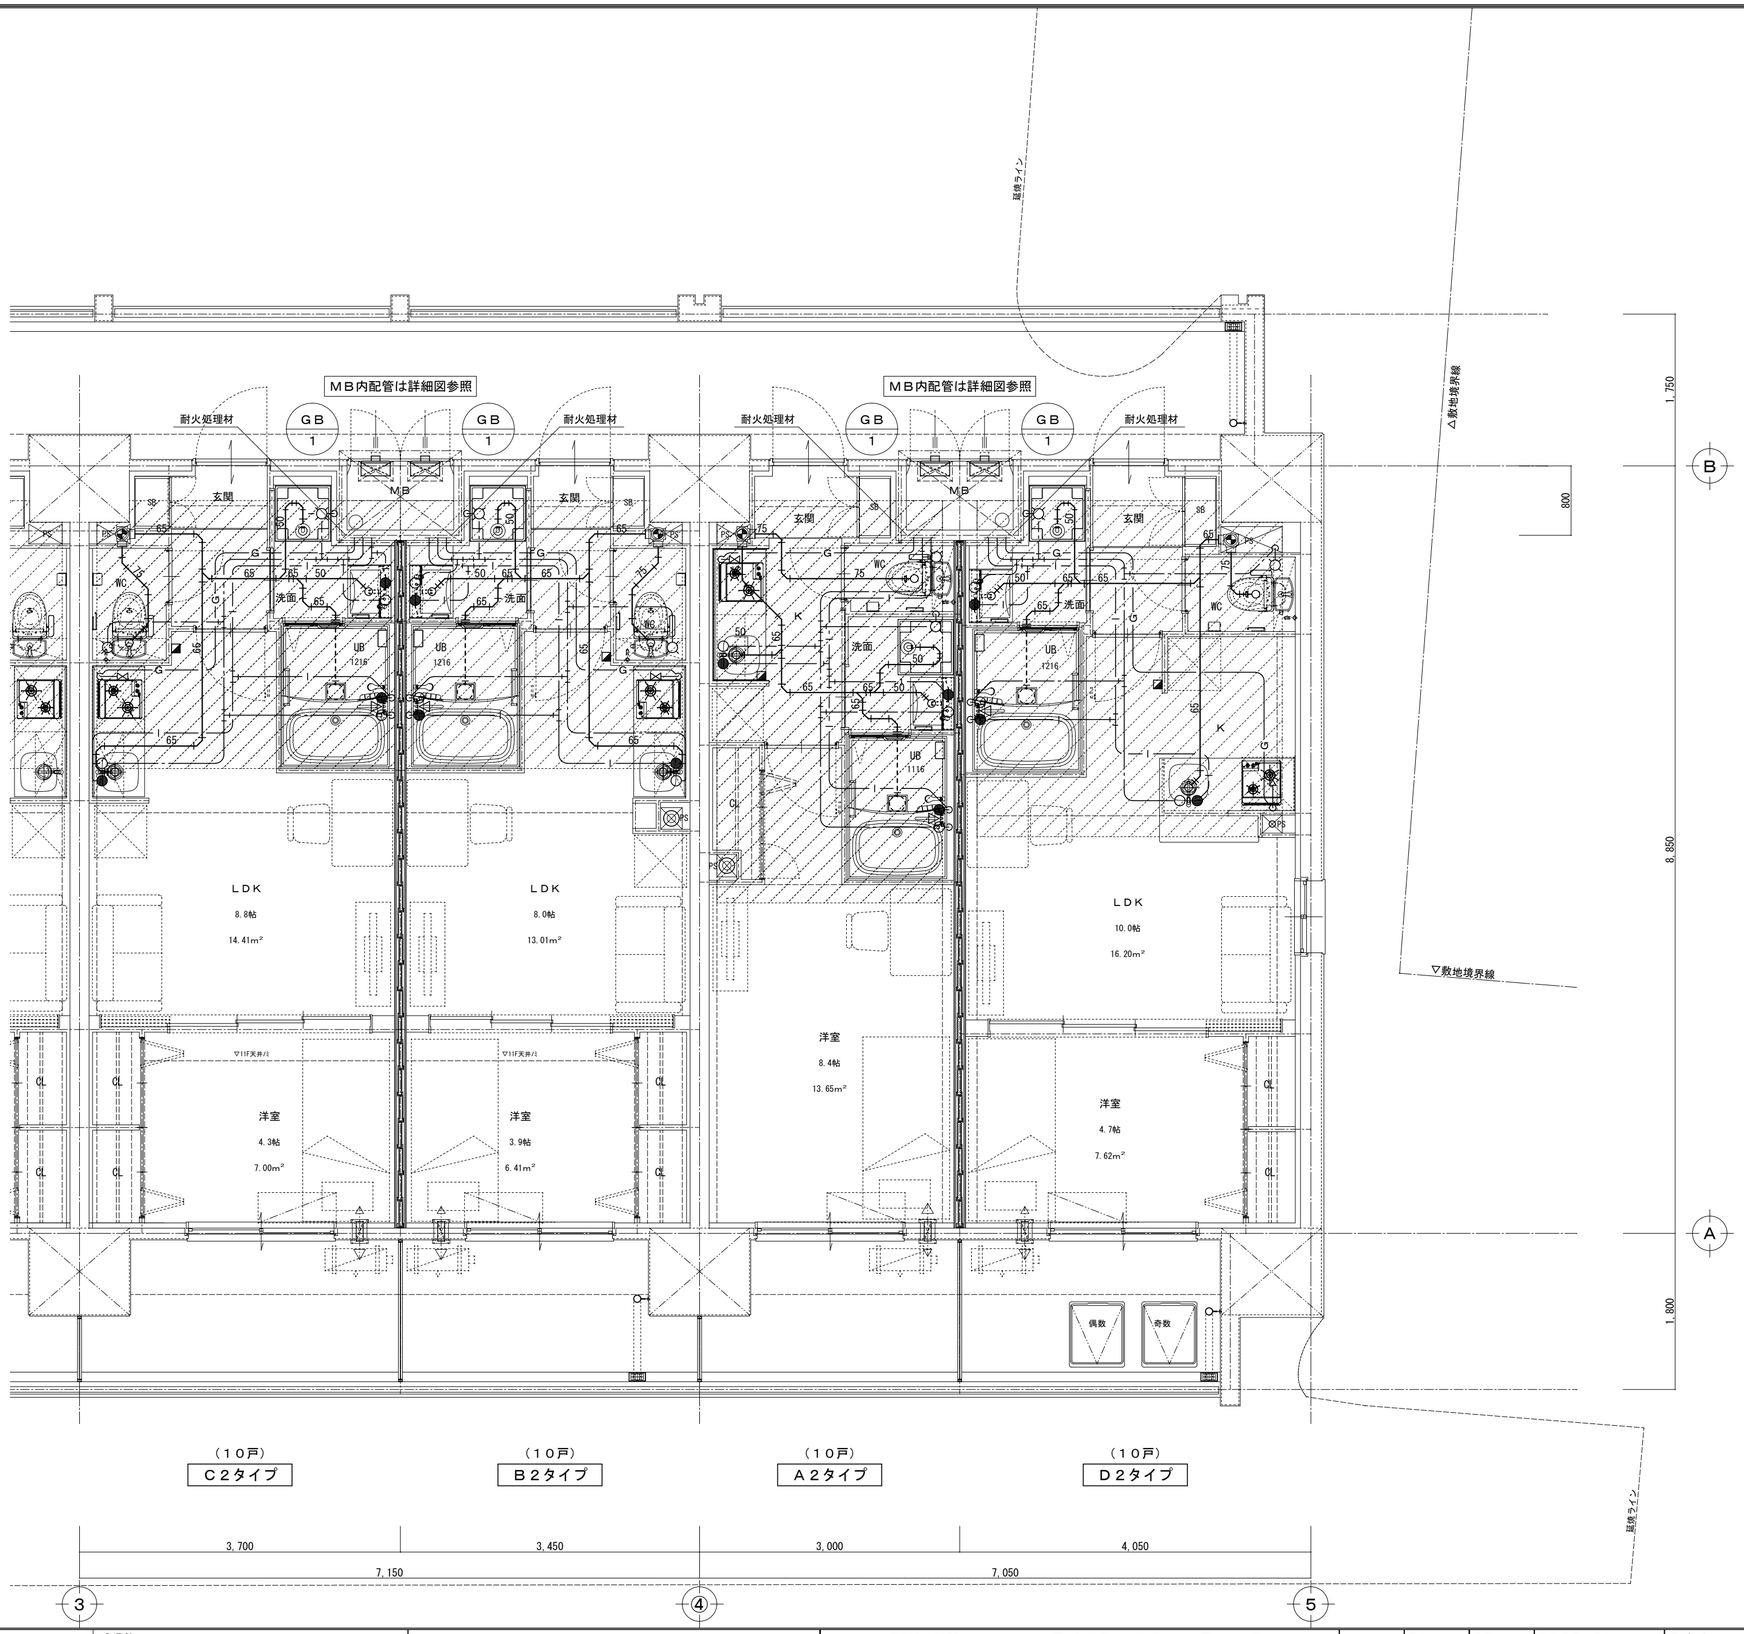

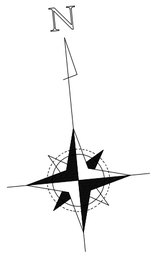

サヤ管先分岐工法　配管サイズ　数字：架橋ポリエチレン管（CD管）	
※　給水管・給湯管　メイン	１６（２８）
※　給湯器	１６（２８）
※　ユニットバス	１３（２２）
※　洗面　洗濯　流し台　便器	１３（２２）
※　ガス管	１５（２８）
※　排水管はコロガシ配管とする。	
◪：給湯器リモコンを示す。	

：コンクリート下り部分を示す

（給排水衛生設備）

２～１１階 住戸平面詳細図（２）　Ｓ＝１：５０

＜性能表示検討項目＞	○温熱－
○構造－	○空気－
○火災－	○光視－
○劣化－	○高齢者－
○維持－	

有限会社 Jib建築設計工舎

〒730－0052　広島市中区千田町３丁目１３番１１号
ＴＥＬ（082）545－8251　ＦＡＸ（082）247－2625
一級建築士事務所　広島県知事登録　第20(1)3419号
一級建築士　大臣登録　第293792号　村上　良彦

PL	DR	DATE（PL）	工事名	図面番号
		DATE（AL）2023.2.15	（仮称）サムティ高松市中央町　新築工事	M－２４
			図面名 ２～１１階 住戸平面詳細図（２）（給排水衛生設備）	SCALE 1／50